LEGEND

●	FOUND SPIKE
●	FOUND ALUMINUM CAP
◉	SET 2" ALUMINUM CAP AVI PC PLS 12045
(R1)	RECORD DATA FROM WIESE SUBDIVISION
(R2)	RECORD DATA FROM MAP OF SURVEY BY JOHN J. STUDLEY PLAT CABINET 6, SLOT 183

NOTES:

- WIESE SUBDIVISION, 2ND FILING CONTAINS 2.30 ACRES ±.
- NO FLOOD HAZARD AREAS ARE WITHIN THE PROPOSED SUBDIVISION (NO BASE FLOOD ELEVATIONS DETERMINED) OF THE SPECIAL FLOOD HAZARD AREA AS SHOWN ON THE FLOOD INSURANCE RATE MAPS FOR LARAMIE COUNTY PANEL 1358 OF 1650. MAP NOS. 56021C1358F WITH AN EFFECTIVE DATE OF JANUARY 17, 2017.
- FIRE PROTECTION WILL BE PROVIDED BY LARAMIE COUNTY FIRE DISTRICT #1.
- WATER AND SEWER SYSTEMS TO BE PROVIDED BY SOUTH CHEYENNE WATER AND SEWER DISTRICT.
- DISTANCES ARE U.S. SURVEY FOOT

BASIS OF BEARINGS

SOUTH LINE OF LOT 3, BLOCK 1 OF WIESE SUBDIVISION BEING MONUMENTED BY FOUND ALUMINUM CAPS AT EACH END. SAID LINE BEARING S89°37'14"E AT A DISTANCE OF 238.41 FEET

COORDINATES SHOWN ARE ARE US STATE PLANE NAD 1983, WYOMING STATE PLANE EAST FIPZONE 4901
TO CONVERT FROM STATE PLANE TO GROUND COORDINATES MULTIPLY BY A PROJECT SCALE FACTOR OF 1.00033589610 AND SUBTRACT 100000 FROM THE NORTHING AND 500000 FROM THE EASTING.

EXAMPLE POINT = POINT OF BEGINNING
STATE PLANE NORTHING = 220834.274
STATE PLANE EASTING = 757357.851
N = (220834.274 x SF)-100000 = 120708.378
E = (757357.851 x SF)-500000 = 257612.018

ORIGINAL FIELD SURVEY BY: AVI PC OCTOBER 2018

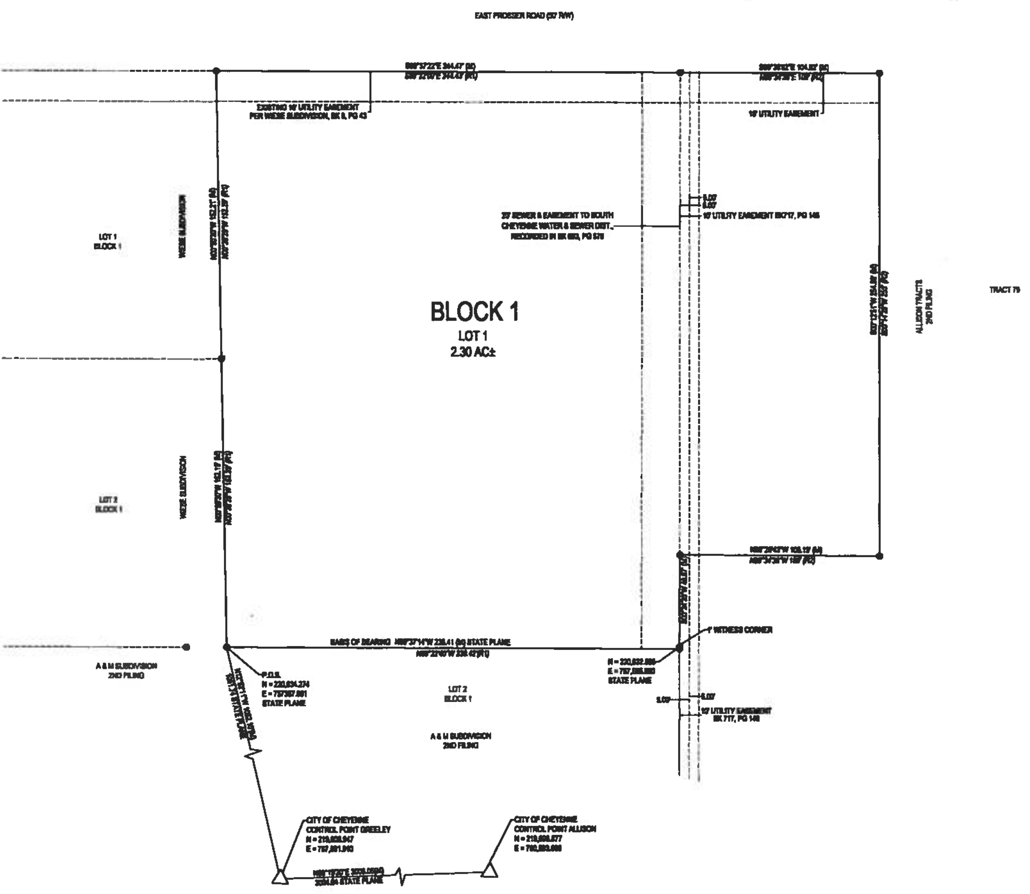

DEDICATION

KNOW ALL MEN BY THESE PRESENTS: THAT MARK CAMPBELL, MANAGER OF PROSSER INVESTORS, LLC., OWNER IN FEE SIMPLE OF THE LAND EMBRACED IN THIS FINAL PLAT OF "WIESE SUBDIVISION, 2ND FILING," DOES HEREBY DECLARE THAT THE SUBDIVISION OF SAID LAND IS WITH HIS FREE ACT AND DEED AND IN ACCORDANCE WITH HIS DESIRES, DOES HEREBY GRANT TO THE PUBLIC THE RIGHTS OF WAY THE EASEMENTS SHOWN HEREON FOR THE PURPOSES INDICATED ON THIS PLAT.

____
MARK CAMPBELL
MANAGER OF PROSSER INVESTORS, LLC

ACKNOWLEDGEMENTS

STATE OF ____________________)
)SS
COUNTY OF __________________)

THE FOREGOING INSTRUMENT WAS ACKNOWLEDGED BEFORE ME BY MARK CAMPBELL, MANAGER OF PROSSER INVESTORS, LLC., THIS ____ DAY OF ______________, 2019, WITNESS MY HAND AND OFFICIAL SEAL.

____
NOTARY PUBLIC, ___________________, WYOMING

MY COMMISSION EXPIRES_________

CERTIFICATE OF SURVEYOR

I, ADAM E. DESCHLER, A PROFESSIONAL LAND SURVEYOR LICENSED IN THE STATE OF WYOMING DO HEREBY CERTIFY THAT THIS PLAT WAS PREPARED FROM THE RECORDS AND FIELD NOTES OF A SURVEY CONDUCTED BY ME OR UNDER MY DIRECT SUPERVISION AND THAT ALL DIMENSIONS AND OTHER DETAILS ARE CORRECT TO THE BEST OF MY KNOWLEDGE AND BELIEF

ADAM E. DESCHLER
12045

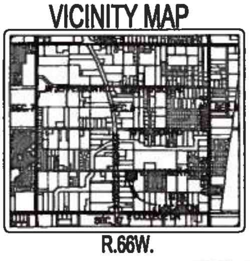

LEGAL DESCRIPTION

A REPLAT OF A PORTION OF TRACT 79 OF ALLISON TRACTS, 2ND FILING, AND LOT 3, BLOCK 1, OF WIESE SUBDIVISION, BEING LOCATED IN A PORTION OF SECTION 8, TOWNSHIP 13 NORTH, RANGE 66 WEST OF THE SIXTH PRINCIPAL MERIDIAN, BEING MORE PARTICULARLY DESCRIBED AS FOLLOWS:

BEGINNING AT THE SOUTHEAST CORNER OF LOT 2, BLOCK 1 OF WIESE SUBDIVISION AND A POINT ON THE NORTH PROPERTY LINE OF LOT 2, BLOCK 1, A&M SUBDIVISION, THENCE ALONG THE EAST PROPERTY LINE OF LOT 2, BLOCK 1, WIESE SUBDIVISION N00°50'30"W A DISTANCE OF 152.19 FEET TO A POINT ON THE EAST PROPERTY LINE OF LOT 1, BLOCK 1, WIESE SUBDIVISION; THENCE ALONG SAID EAST PROPERTY LINE OF LOT 1, BLOCK 1, WIESE SUBDIVISION, N00°50'30"W A DISTANCE OF 152.21 FEET TO A POINT ON THE SOUTH RIGHT OF WAY LINE OF EAST PROSSER ROAD; THENCE ALONG SAID SOUTH RIGHT OF WAY LINE OF EAST PROSSER ROAD S89°37'22"E A DISTANCE OF 244.47 TO A POINT; THENCE CONTINUING ALONG SAID SOUTH RIGHT OF WAY LINE OF EAST PROSSER ROAD S89°36'52"E A DISTANCE OF 104.92 FEET TO A POINT; THENCE S00°12'51"W A DISTANCE OF 254.98 FEET TO A POINT; THENCE N89°28'43"W A DISTANCE OF 108.19 FEET TO A POINT; THENCE S00°24'36"W A DISTANCE OF 49.87 FEET TO A POINT ON THE NORTH PROPERTY LINE OF SAID LOT 2, BLOCK 1, A&M SUBDIVISION; THENCE ALONG SAID NORTH PROPERTY LINE OF LOT 2, BLOCK 1, A&M SUBDIVISION N89°37'14"W A DISTANCE OF 238.41 MORE OR LESS TO THE POINT OF BEGINNING.

SAID PARCEL OF LAND CONTAINS 2.30 ACRES MORE OR LESS

APPROVALS

APPROVED BY THE CHEYENNE PLANNING COMMISSION THIS _____ DAY OF________________ 20___

____
DEVELOPMENT DIRECTOR

APPROVED BY THE CITY COUNCIL OF THE CITY OF CHEYENNE, THIS _____ DAY OF ________________ 20___

______________________________ MAYOR
______________________________ CITY CLERK

APPROVALS

APPROVED BY THE LARAMIE COUNTY PLANNING COMMISSION THIS _____ DAY OF________________, 20___

____
CHAIR PERSON FOR THE PLANNING COMMISSION

APPROVED BY THE COUNTY COMMISSIONERS OF LARAMIE COUNTY, WYOMING THIS _____ DAY OF ________________, 20___

______________________________ CHAIR PERSON, BOARD OF COUNTY COMMISSIONERS
______________________________ COUNTY CLERK

SCALE 1" = 60'

FINAL PLAT FOR WIESE SUBDIVISION 2ND FILING

A REPLAT OF A PORTION OF TRACT 79, ALLISON TRACTS, 2ND FILING AND LOT 3, BLOCK 1, WIESE SUBDIVISION, BEING SITUATED IN A PORTION OF SECTION 8, TOWNSHIP 13 NORTH, RANGE 66 WEST, OF THE 6TH PRINCIPAL MERIDIAN, LARAMIE COUNTY, WYOMING
PREPARED NOVEMBER 2018

NO.	REVISION	DATE
1	SUBMITTAL	11 30 18
2	REVIEW COMMENTS	1 14 19

PREPARED FOR:
PROSSER INVESTORS, LLC
5613 DTC PARKWAY STE 810
GREENWOOD VILLAGE, CO 80110

PROJECT:
WIESE SUBDIVISION, 2ND FILING

DRAWING TITLE:
FINAL PLAT

AVI
ENGINEERING
PLANNING
SURVEYING

307.637.6017
1103 OLD TOWN LANE, SUITE 101
CHEYENNE, WY 82009
AVI@AVIPC.COM

DATE:	Jan 14, 2019
DRAWN BY:	BMH
DESIGNED BY:	BMH
CHECKED BY:	AD
JOB NO.:	4189
DRAWING NO.	1 OF 1