
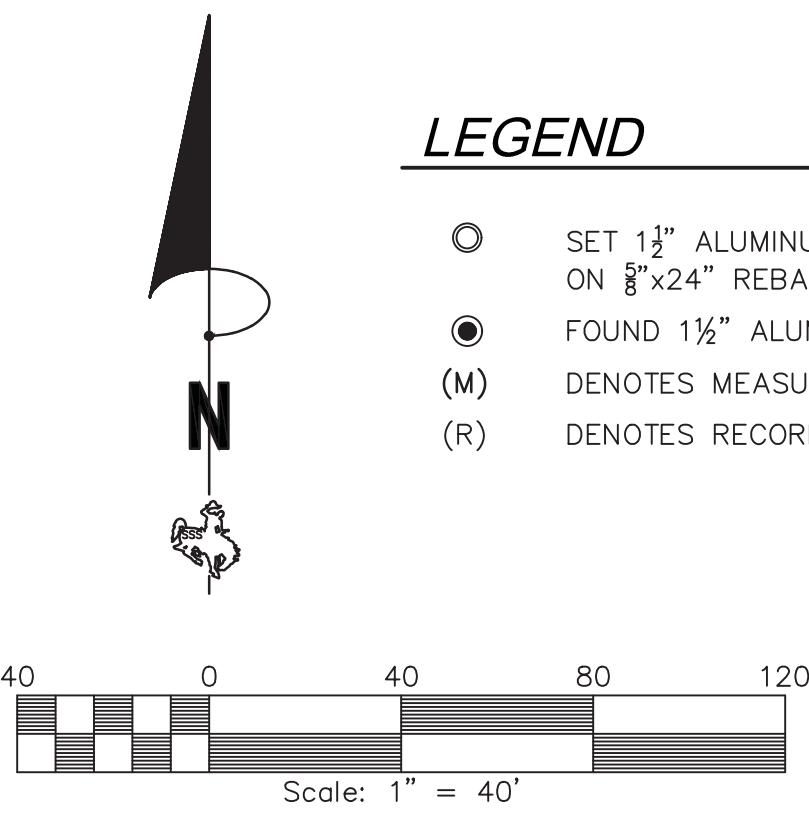


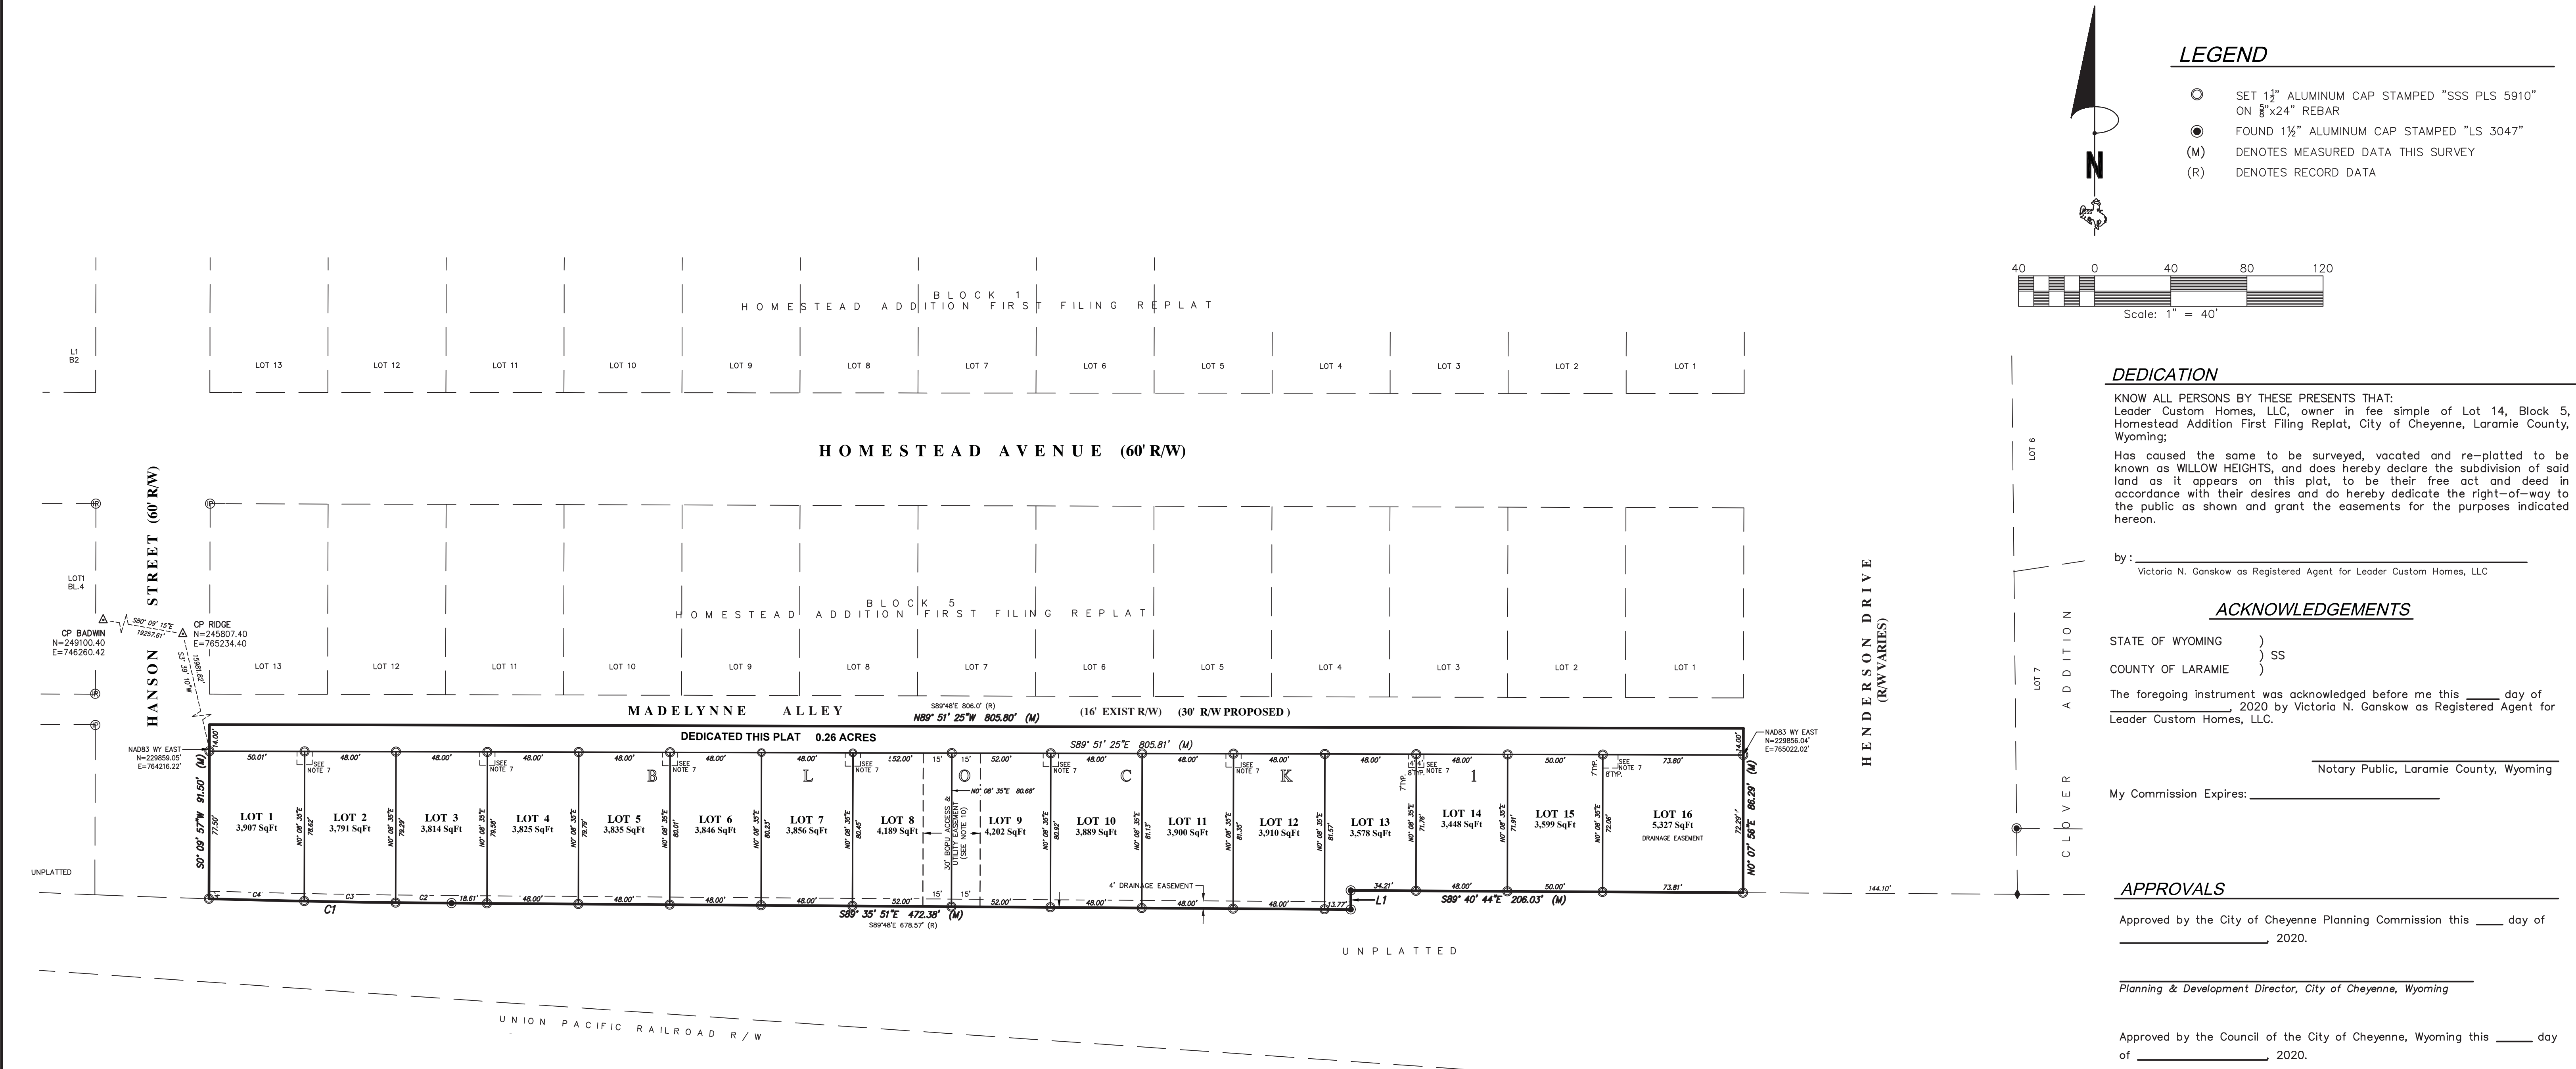

- LEGEND**
- SET 1½" ALUMINUM CAP STAMPED "SSS PLS 5910" ON ⅝"x24" REBAR
 - FOUND 1½" ALUMINUM CAP STAMPED "LS 3047"
 - (M) DENOTES MEASURED DATA THIS SURVEY
 - (R) DENOTES RECORD DATA

DEDICATION

KNOW ALL PERSONS BY THESE PRESENTS THAT: Leader Custom Homes, LLC, owner in fee simple of Lot 14, Block 5, Homestead Addition First Filing Replat, City of Cheyenne, Laramie County, Wyoming;

Has caused the same to be surveyed, vacated and re-platted to be known as WILLOW HEIGHTS, and does hereby declare the subdivision of said land as it appears on this plat, to be their free act and deed in accordance with their desires and do hereby dedicate the right-of-way to the public as shown and grant the easements for the purposes indicated hereon.

by : Victoria N. Ganskow as Registered Agent for Leader Custom Homes, LLC

ACKNOWLEDGEMENTS

STATE OF WYOMING)
COUNTY OF LARAMIE) SS

The foregoing instrument was acknowledged before me this ____ day of _____, 2020 by Victoria N. Ganskow as Registered Agent for Leader Custom Homes, LLC.

Notary Public, Laramie County, Wyoming

My Commission Expires: _____

APPROVALS

Approved by the City of Cheyenne Planning Commission this ____ day of _____, 2020.


Planning & Development Director, City of Cheyenne, Wyoming

Approved by the Council of the City of Cheyenne, Wyoming this ____ day of _____, 2020.

Mayor City Clerk

CERTIFICATE OF SURVEYOR


I, Jeffrey B. Jones, Licensed Professional Land Surveyor in the State of Wyoming, for and on behalf of Steil Surveying Services, LLC, hereby state, to the best of my knowledge, information and belief, that this map was prepared from field notes taken during an actual survey made by me or under my direct supervision; and that this map correctly shows the results of said survey and that the monuments found or set are as shown.

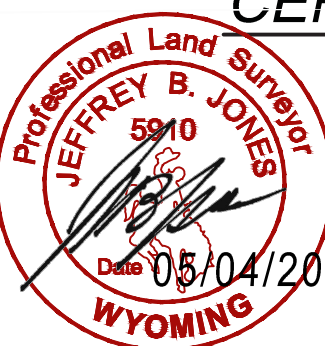

WILLOW HEIGHTS

A REPLAT OF LOT 14, BLOCK 5
HOMESTEAD ADDITION, FIRST FILING REPLAT
CITY OF CHEYENNE,
LARAMIE COUNTY, WYOMING

PREPARED SEPTEMBER 2019

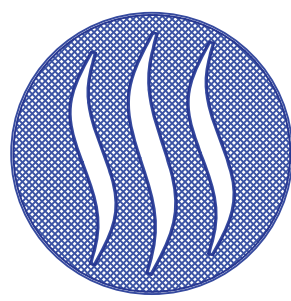

STEIL SURVEYING SERVICES, LLC
PROFESSIONAL LAND SURVEYORS
PLANNING & DEVELOPMENT SPECIALISTS
1102 WEST 19th ST. CHEYENNE, WY. 82001 o (307) 634.7273
756 GILCHRIST ST. WHEATLAND, WY. 82201 o (307) 322.9789
www.SteilSurvey.com o info@SteilSurvey.com

CURVE TABLE					
CURVE #	DELTA	RADIUS	CHORD BEARING	CHORD LENGTH	ARC LENGTH
C1	1° 17' 08"	5679.65'	N88° 57' 40"W	127.44'	127.45'
C1(R)	—	5679.65'	—	127.57'	—
C2	0° 17' 47"	5679.65'	N89° 27' 21"W	29.39'	29.39'
C3	0° 29' 03"	5679.65'	N89° 03' 55"W	48.00'	48.00'
C4	0° 30' 18"	5679.65'	N88° 34' 15"W	50.05'	50.05'

LINE TABLE		
Line #	Bearing	Length
L1	N0° 15' 10"E	9.98'
L1(R)	N0° 12"E	10.0'

NOTES

1. BASIS OF BEARINGS — WYOMING STATE PLANE COORDINATES, EAST ZONE — NAD83—2011. SITE COMBINATION FACTOR = 0.99996657156.
2. ALL UNMONUMENTED LOT CORNERS, ANGLE POINTS, AND POINTS OF CURVATURE TO BE MONUMENTED WITH 1½" ALUMINUM CAP STAMPED "SSS P.L.S. 5910" ON ⅝"x24" REBAR.
3. NO PORTION OF THE PROPERTY AS SHOWN FALLS WITHIN A F.E.M.A. 100-YEAR SPECIAL FLOOD HAZARD AREA AS SHOWN ON JANUARY 17, 2007 F.I.R.M. PANEL No. 56021C1094F (09/27/12).
4. DOMESTIC WATER AND SANITARY SEWER SERVICES TO BE PROVIDED BY CITY OF CHEYENNE BOARD OF PUBLIC UTILITIES (BOPU).
5. PUBLIC GREENWAY: LOT 16, BLOCK 1 HEREON IS HEREBY GRANTED AS A DRAINAGE EASEMENT AND DEDICATED AS PUBLIC GREENWAY AND SHALL BE OWNED & MAINTAINED BY THE CITY OF CHEYENNE, FLOODPLAIN & GREENWAY ADMINISTRATOR (SEE NOTE TO ASSESSOR).
6. ALL UTILITIES TO BE PROVIDED IN PUBLIC RIGHT(S)-OF-WAY OR EASEMENTS AS SHOWN AND DESCRIBED HEREON.
7. "BHE EASEMENTS" SHOWN HEREON (7'W x 8'D) GRANTED TO BLACK HILLS ENERGY, THEIR LEGAL SUCCESSORS AND/OR ASSIGNS FOR THE PROVISION OF LOCAL SERVICE LINES & PEDESTAL(S) ONLY — PEDESTALS MUST BE SETBACK A MINIMUM OF 4' FROM THE PUBLIC R/W LINE OF "MADELYNNE ALLEY" (30' R/W).
8. LANDS CONTAINED WITHIN THE PLAT BOUNDARY ARE SUBJECT TO THE PROVISIONS OF THE "WILLOW HEIGHTS DEVELOPMENT AGREEMENT"; (CITY CONTRACT # _____) RECORDED _____ IN THE REAL ESTATE OFFICE OF THE CLERK OF LARAMIE COUNTY, WYOMING AT BOOK ____ PAGE _____.
9. 4' PEDESTRIAN RIGHT-OF-WAY EASEMENT GRANTED HEREON TO BE CONSIDERED AND REGARDED AS PUBLIC RIGHT-OF-WAY UNDER AUTHORITY OF THE CITY OF CHEYENNE.
10. BOARD OF PUBLIC UTILITIES (BOPU) ACCESS & UTILITY EASEMENT(S) :
 - a. THOSE BOPU ACCESS & UTILITY EASEMENT(S) (HEREINAFTER REFERRED TO AS "BOPU EASEMENT(S)"), AS SHOWN AND DESCRIBED HEREON, ARE HEREBY GRANTED TO THE BOARD OF PUBLIC UTILITIES OF THE CITY OF CHEYENNE (BOPU), THEIR LEGAL SUCCESSORS AND/OR ASSIGNS, FOR INSTALLATION, MAINTENANCE, REPAIR, ALTERATION AND OPERATION OF SANITARY SEWER MAINS/PIPELINES (FACILITIES).
 - NO OTHER UTILITIES MAY INSTALL FACILITIES ON OR WITHIN THE BOPU UTILITY EASEMENT, EXCEPT AS FOLLOWS:
 - i. OTHER UTILITIES MAY CROSS THE BOPU UTILITY EASEMENT, IF AND ONLY IF:
 - ii. UTILITY'S FACILITIES CROSS THE BOPU FACILITIES AT NO LESS THAN A 60 DEGREE ANGLE;
 - iii. A MINIMUM OF 24 INCHES OF VERTICAL CLEARANCE IS PROVIDED BETWEEN THE BOPU FACILITIES AND THE CROSSING FACILITIES, UNLESS OTHERWISE APPROVED BY THE BOPU; AND
 - iv. A COPY OF ANY UTILITY EASEMENT AUTHORIZING THE CROSSING OF THE BOPU UTILITY EASEMENT IS PROVIDED TO THE BOPU PRIOR TO ANY CONSTRUCTION WITHIN THE BOPU UTILITY EASEMENT.
 - c. IF GRANTOR REQUIRES RELOCATION OF THE FACILITIES, GRANTEE AGREES TO RELOCATE THE FACILITIES PROVIDED THAT GRANTOR PAYS FOR THE RELOCATION OF THE FACILITIES, PROVIDES A SUITABLE ALTERNATE LOCATION FOR SUCH FACILITIES AND GRANTS THE NECESSARY EASEMENT RIGHTS AT THE NEW LOCATION UPON THE SAME TERMS AND CONDITIONS PROVIDED WITH THE ORIGINAL EASEMENT.
 - d. IF GRANTEE (BOPU/CITY OF CHEYENNE) REQUIRES RELOCATION OF THE FACILITIES, GRANTEE SHALL PAY FOR REMOVAL AND RELOCATION OF THE FACILITIES.
 - e. IF GRANTEE ACCESSES THE FACILITIES OR UNDERTAKES WORK OR MAINTENANCE ON THE FACILITIES, GRANTEE SHALL REPAIR ANY DAMAGE TO GRANTOR'S PROPERTY RESULTING THEREFROM; INCLUDING RESTORATION OF ANY AREAS DISTURBED AS A RESULT OF SUCH ACCESS AND/OR WORK.

NOTE TO ASSESSOR


OWNERS OF THE LANDS CONTAINED WITHIN THIS PLAT, BY WAY OF THEIR PREVIOUS DEEDED OWNERSHIP AND THEIR SIGNATURES AFFIXED HEREON HEREBY CERTIFY THAT BY THEIR FREE ACT AND DEED AND IN ACCORDANCE WITH THEIR DESIRES, THE OWNERSHIP OF LOTS CONTAINED WITHIN THIS PLAT SHALL BE AS FOLLOWS:

CITY OF CHEYENNE — LOT 16
LEADER CUSTOM HOMES, LLC — LOTS 1 THRU 15

AS REQUIRED BY LARAMIE COUNTY, FOLLOWING THE RECORDING OF THIS PLAT, LEGAL CONVEYANCE OF THE INDIVIDUAL OWNERSHIP(S)/INTEREST(S) NOTED ABOVE REQUIRES THAT ALL STAKEHOLDERS RECORD AN APPROPRIATE INSTRUMENT MEETING THE FORM ESTABLISHED IN W.S. § 34-2 et seq.

VACATION STATEMENT

IT IS THE INTENT OF THIS REPLAT TO VACATE ALL OF LOT 14, BLOCK 5, HOMESTEAD ADDITION, FIRST FILING REPLAT, LARAMIE COUNTY, WYOMING, INCLUDING ALL LOT LINES AND EASEMENTS OF RECORD

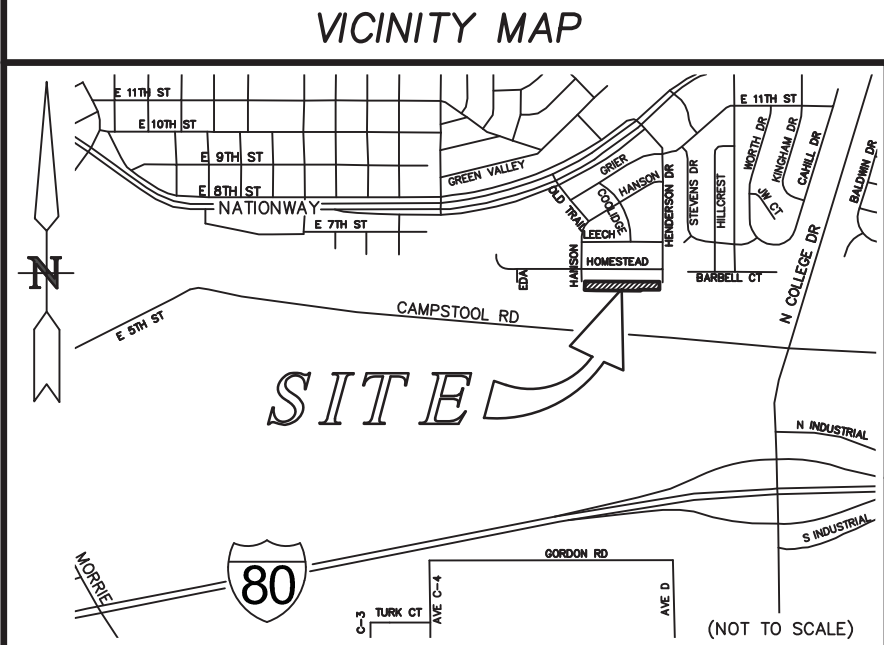

FILING RECORD

REVISED: 05/04/2020

~SSS\18084 Gonskow\18084 WILLOW HEIGHTS FINAL.dwg

© COPYRIGHT 2020 STEIL SURVEYING SERVICES, LLC ALL RIGHTS RESERVED