

▫ DOMESTIC WATER & SANITARY SEWER PROVIDED BY CITY OF CHEYENNE BOPU ▫ THE SURFACE ESTATE OF THE LAND TO BE SUBDIVIDED IS SUBJECT TO FULL AND EFFECTIVE DEVELOPMENT OF THE MINERAL ESTATE ▫

GENERAL NOTES

- 1) THIS SURVEY DOES NOT CONSTITUTE A TITLE SEARCH BY ANTELOPE SURVEYING, INC. TO DETERMINE RECORD TITLE, EASEMENTS OR RIGHTS-OF-WAY. TITLE COMMITMENT NO. 995820CHE, WITH AN EFFECTIVE DATED OF AUGUST 2, 2021 AND TITLE COMMITMENT NO. 995830CHE, WITH AN EFFECTIVE DATE OF AUGUST 2, 2021, BOTH PREPARED BY LARAMIE COUNTY ABSTRACT AND TITLE COMPANY WAS RELIED UPON FOR ALL INFORMATION REGARDING TITLE OF RECORD, EASEMENTS OF RECORD AND RIGHTS-OF-WAY.
- 2) BEARINGS SHOWN HEREON ARE ASSUMED AND ARE BASED UPON THE NORTH LINE OF LOTS 8 THROUGH 12, INCLUSIVE, KORNEGAY HOMESITES, COUNTY OF LARAMIE, STATE OF WYOMING, PER THE PLAT RECORDED NOVEMBER 6, 1946 AT RECEPTION NO. 453298 IN THE COUNTY CLERK'S OFFICE FOR LARAMIE COUNTY, STATE OF WYOMING, WHICH BEARS SOUTH 89°43'20" EAST BETWEEN THE MONUMENTS SHOWN HEREON.
- 3) BY SCALED MAP LOCATION AND GRAPHIC PLOTTING ONLY, THIS PROPERTY LIES IN ZONE X OF THE FLOOD INSURANCE RATE MAP, COMMUNITY PANEL NUMBER 56021C1087F AND DATED JANUARY 17, 2007 - SUBJECT PROPERTY IS NOT IN A SPECIAL FLOOD HAZARD AREA.
- 4) FIELD WORK FOR THIS SURVEY WAS PERFORMED ON JULY 29 & 30, 2021.
- 5) THE LINEAL UNITS OF MEASURE SHOWN ON THIS SURVEY ARE BASED UPON THE U.S. SURVEY FOOT.
- 6) ALL NORTHINGS AND EASTINGS, AS SHOWN ON THIS PLAT, ARE BASED UPON THE NORTH AMERICAN DATUM OF 1983 (NAD 83), WYOMING STATE PLANE COORDINATES, EAST ZONE.

LINE LEGEND

- = SUBJECT PARCEL BOUNDARY LINES
= SECTION LINES
= ADJOINING PARCEL BOUNDARY LINES
= EXISTING EASEMENT LINES
= EASEMENT LINES CREATED BY THIS PLAT

MONUMENT NOTES


- INDICATES FOUND MONUMENT AS NOTED
○ INDICATES SET MONUMENT STAMPED "STAMPADOS PLS 6956"

MISCELLANEOUS NOTES

- (R) INDICATES RECORD INFORMATION PER THE PLAT OF KORNEGAY HOMESITES RECORDED NOVEMBER 6, 1946 AT RECEPTION NO. 453298.
(M) INDICATES MEASURED BEARINGS AND DISTANCES

TRACT 3
STOREY ACRES

LINE TABLE		
LINE	BEARING	LENGTH
L1	S48°51'43"E	6.13'
L2	S00°04'50"E	20.00'

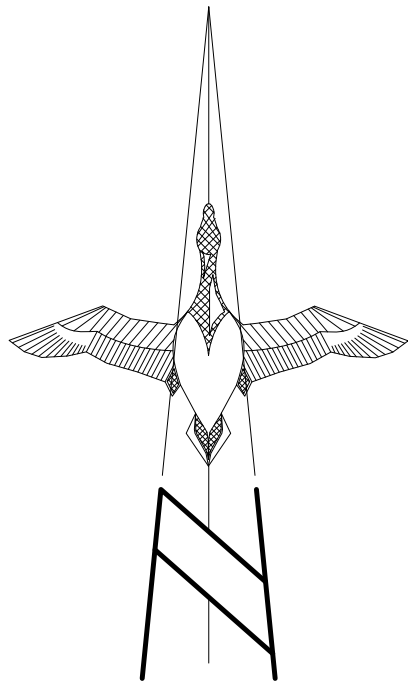

DEDICATION

KNOW ALL PERSONS BY THESE PRESENTS THAT: JP MORGAN CHASE BANK, N.A. OWNER IN FEE SIMPLE OF LOTS 8, 9, 10, 11 AND 12, KORNEGAY HOMESITES, COUNTY OF LARAMIE, STATE OF WYOMING.

HAVE CAUSED THE SAME TO BE SURVEYED, VACATED AND RE-PLATTED TO BE KNOWN AS KORNEGAY HOMESITES, 3RD FILING AND DOES HEREBY DECLARE THE SUBDIVISION OF SAID LAND AS IT APPEARS ON THIS PLAT, TO BE THEIR FREE ACT AND DEED AND IN ACCORDANCE WITH THEIR DESIRES.

OWNER: JPMORGAN CHASE BANK, N.A.

BY: _____
RONALD CHESTER AS VICE PRESIDENT

ACKNOWLEDGEMENT

STATE OF _____)
COUNTY OF _____)SS

THE FORGOING INSTRUMENT WAS ACKNOWLEDGED BEFORE ME THIS ____ DAY OF _____ 2021, BY RONALD CHESTER AS VICE PRESIDENT FOR JPMORGAN CHASE BANK, N.A.


NOTARY PUBLIC, LARAMIE COUNTY, WYOMING

MY COMMISSION EXPIRES: _____

CERTIFICATE OF SURVEYOR

I, WILLIAM C. STAMPADOS, A PROFESSIONAL LAND SURVEYOR IN THE STATE OF WYOMING, FOR AND ON BEHALF OF ALTURA LAND CONSULTANTS, LLC, HEREBY STATE, TO THE BEST OF MY KNOWLEDGE, INFORMATION AND BELIEF, THAT THIS MAP WAS PREPARED FROM FIELD NOTES TAKEN DURING AN ACTUAL SURVEY MADE BY ME OR UNDER MY DIRECT SUPERVISION; AND THAT THIS MAP CORRECTLY SHOWS THE RESULTS OF SAID SURVEY AND THAT THE MONUMENTS FOUND OR SET ARE AS SHOWN.

WILLIAM C. STAMPADOS, PLS 6956
WYOMING LICENSED PROFESSIONAL LAND SURVEYOR
FOR AND ON THE BEHALF OF ANTELOPE SURVEYING, INC.

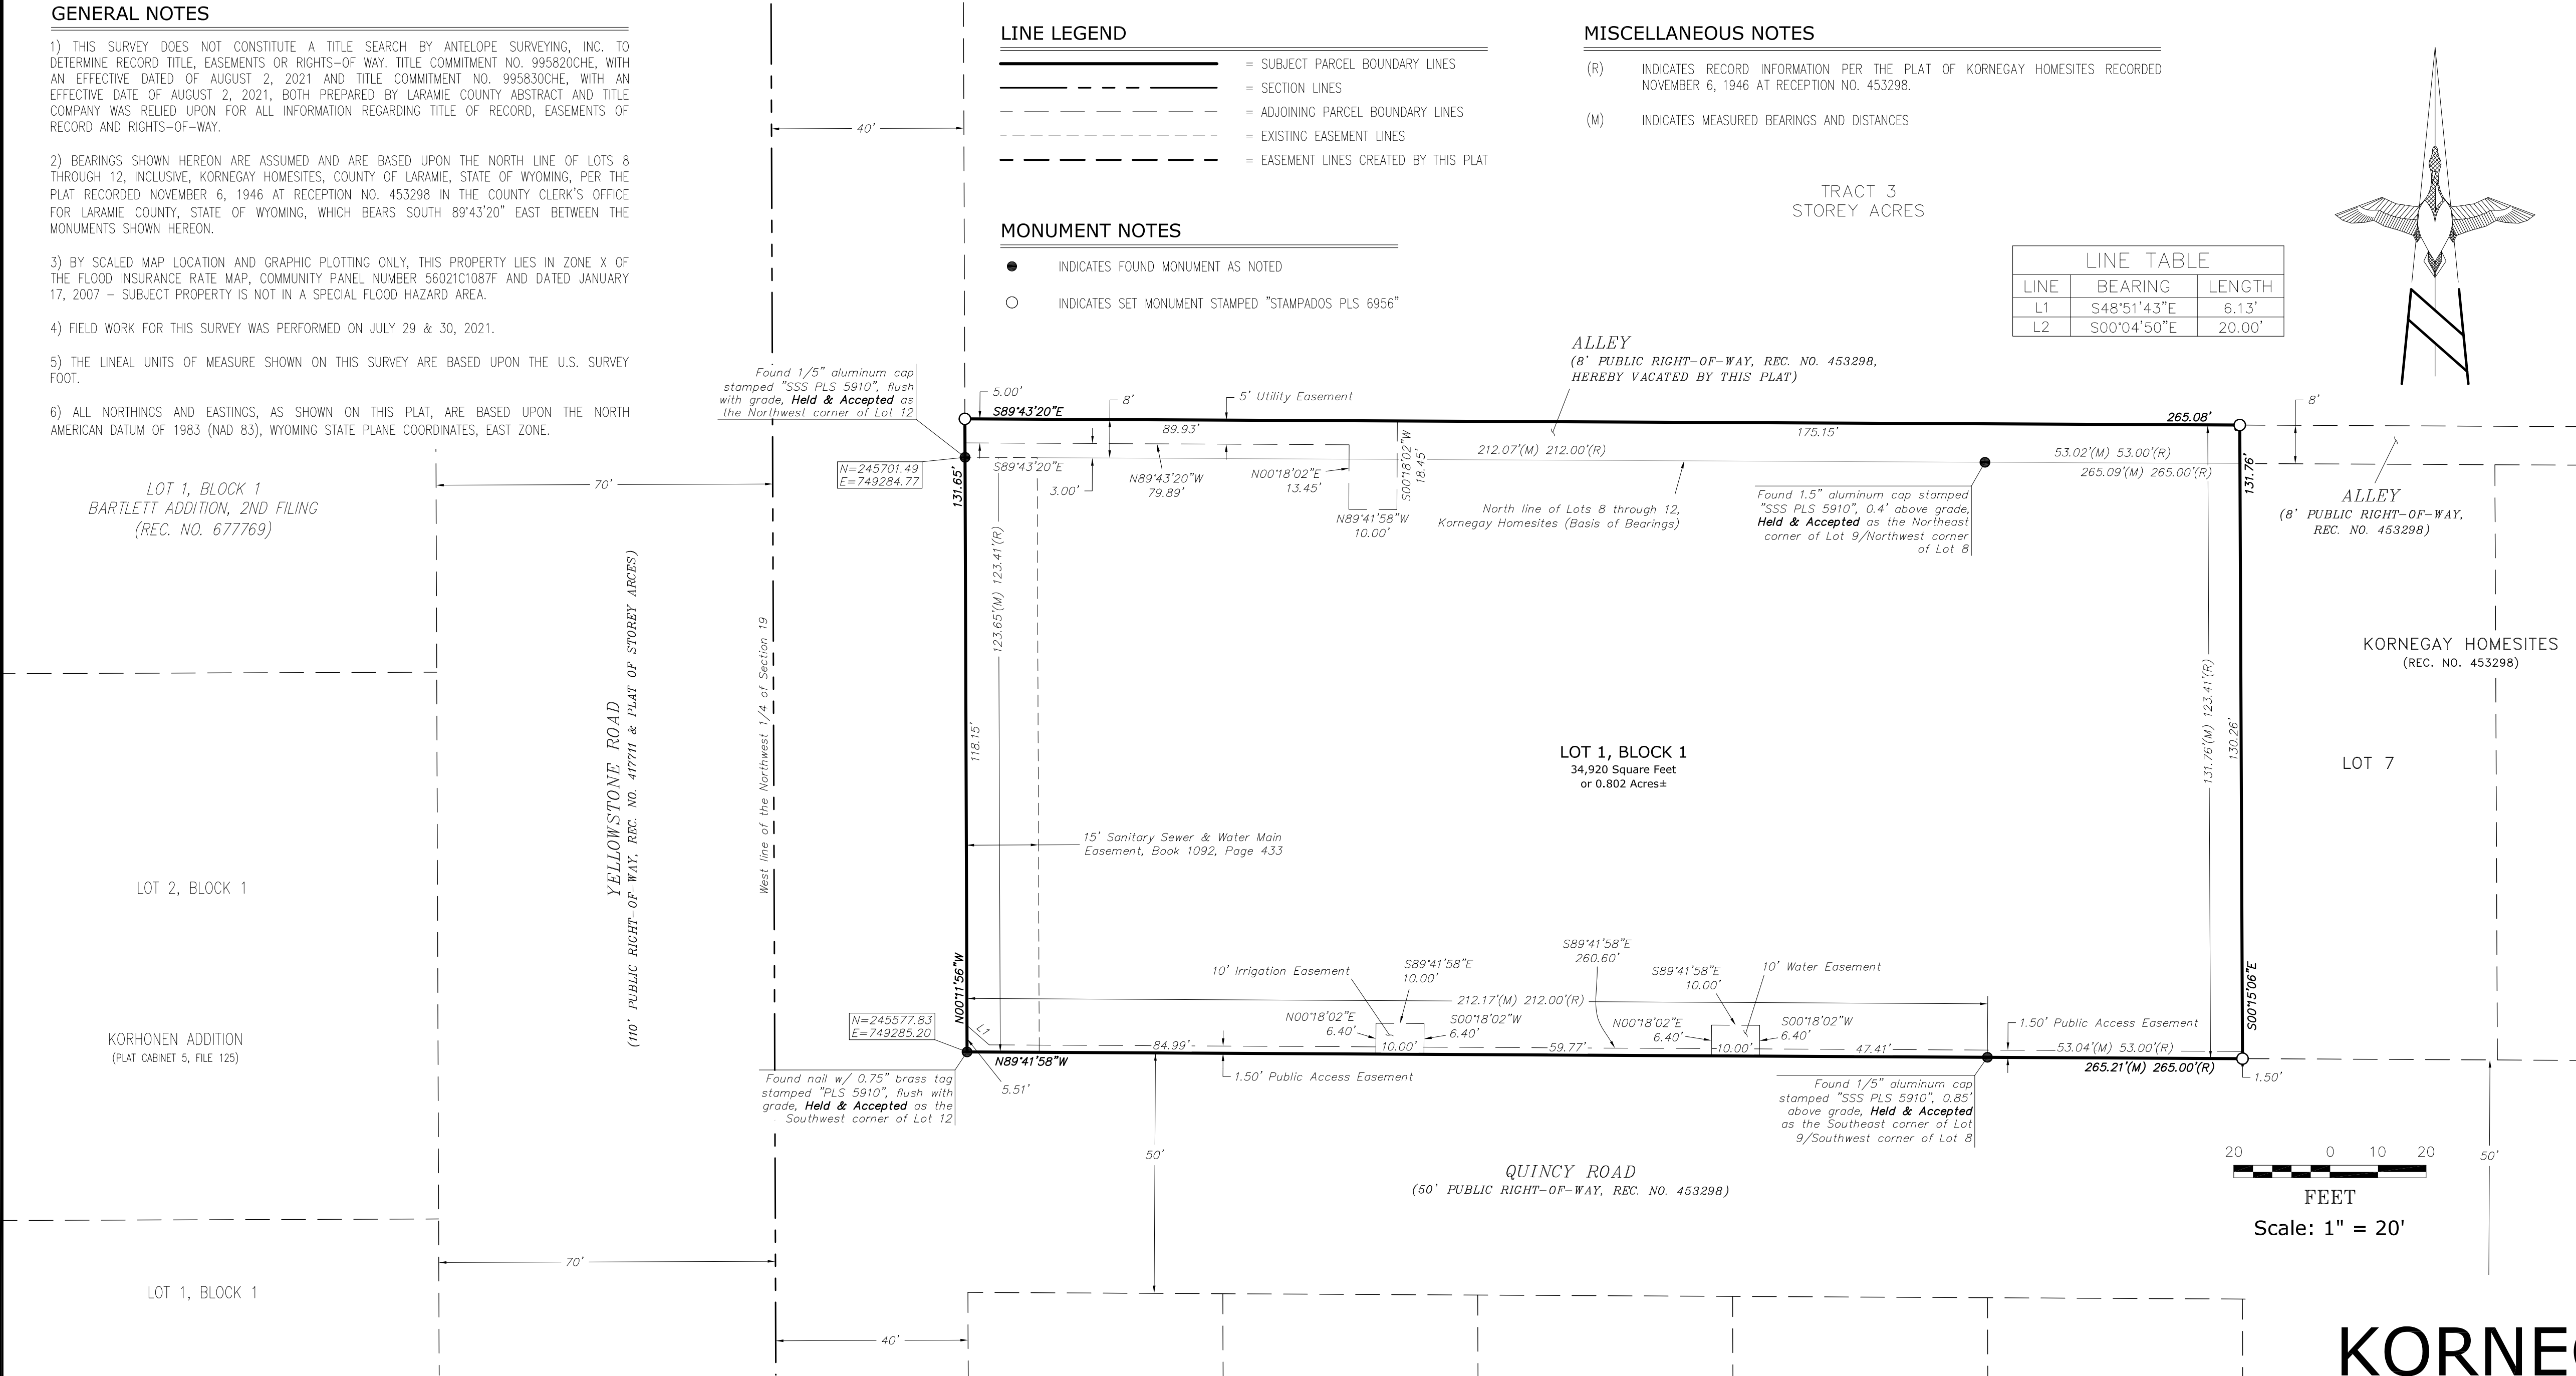

VACATION STATEMENT

IT IS THE INTENT OF THIS REPLAT TO VACATE ALL OF LOTS 8 THROUGH 12, INCLUSIVE AND 8-FOOT-WIDE ALLEY DIRECTLY NORTH AND ADJACENT TO LOTS 8 THROUGH 12, INCLUSIVE, KORNEGAY HOMESITES, LARAMIE COUNTY, WYOMING.

VICINITY MAP



APPROVALS

APPROVED BY THE CITY OF CHEYENNE PLANNING COMMISSION THIS ____ DAY OF _____ 2021.

PLANNING & DEVELOPMENT DIRECTOR, CITY OF CHEYENNE, WYOMING

APPROVED BY THE COUNCIL OF THE CITY OF CHEYENNE, WYOMING THIS ____ DAY OF _____, 2021.

MAYOR _____ ATTEST: _____
CITY CLERK

FILING RECORD

KORNEGAY HOMESITES, 3RD FILING

A REPLAT OF LOTS 8 THROUGH 12, INCLUSIVE, AND 8' ALLEY DIRECTLY NORTH AND ADJACENT TO LOTS 8 THROUGH 12, INCLUSIVE, KORNEGAY HOMESITES

LYING WITHIN THE NORTHWEST 1/4 OF SECTION 19, TOWNSHIP 14 NORTH, RANGE 66 WEST OF THE 6TH PRINCIPAL MERIDIAN, COUNTY OF LARAMIE, STATE OF WYOMING

Antelope Surveying, Inc.

Firm Registration #2017-000778867
4903 South Fox Street
Englewood, Colorado 80110
Phone: (303) 748-2181



THIS SUBDIVISION PLAT WAS PREPARED
ON THE 15TH DAY OF SEPTEMBER, 2021